


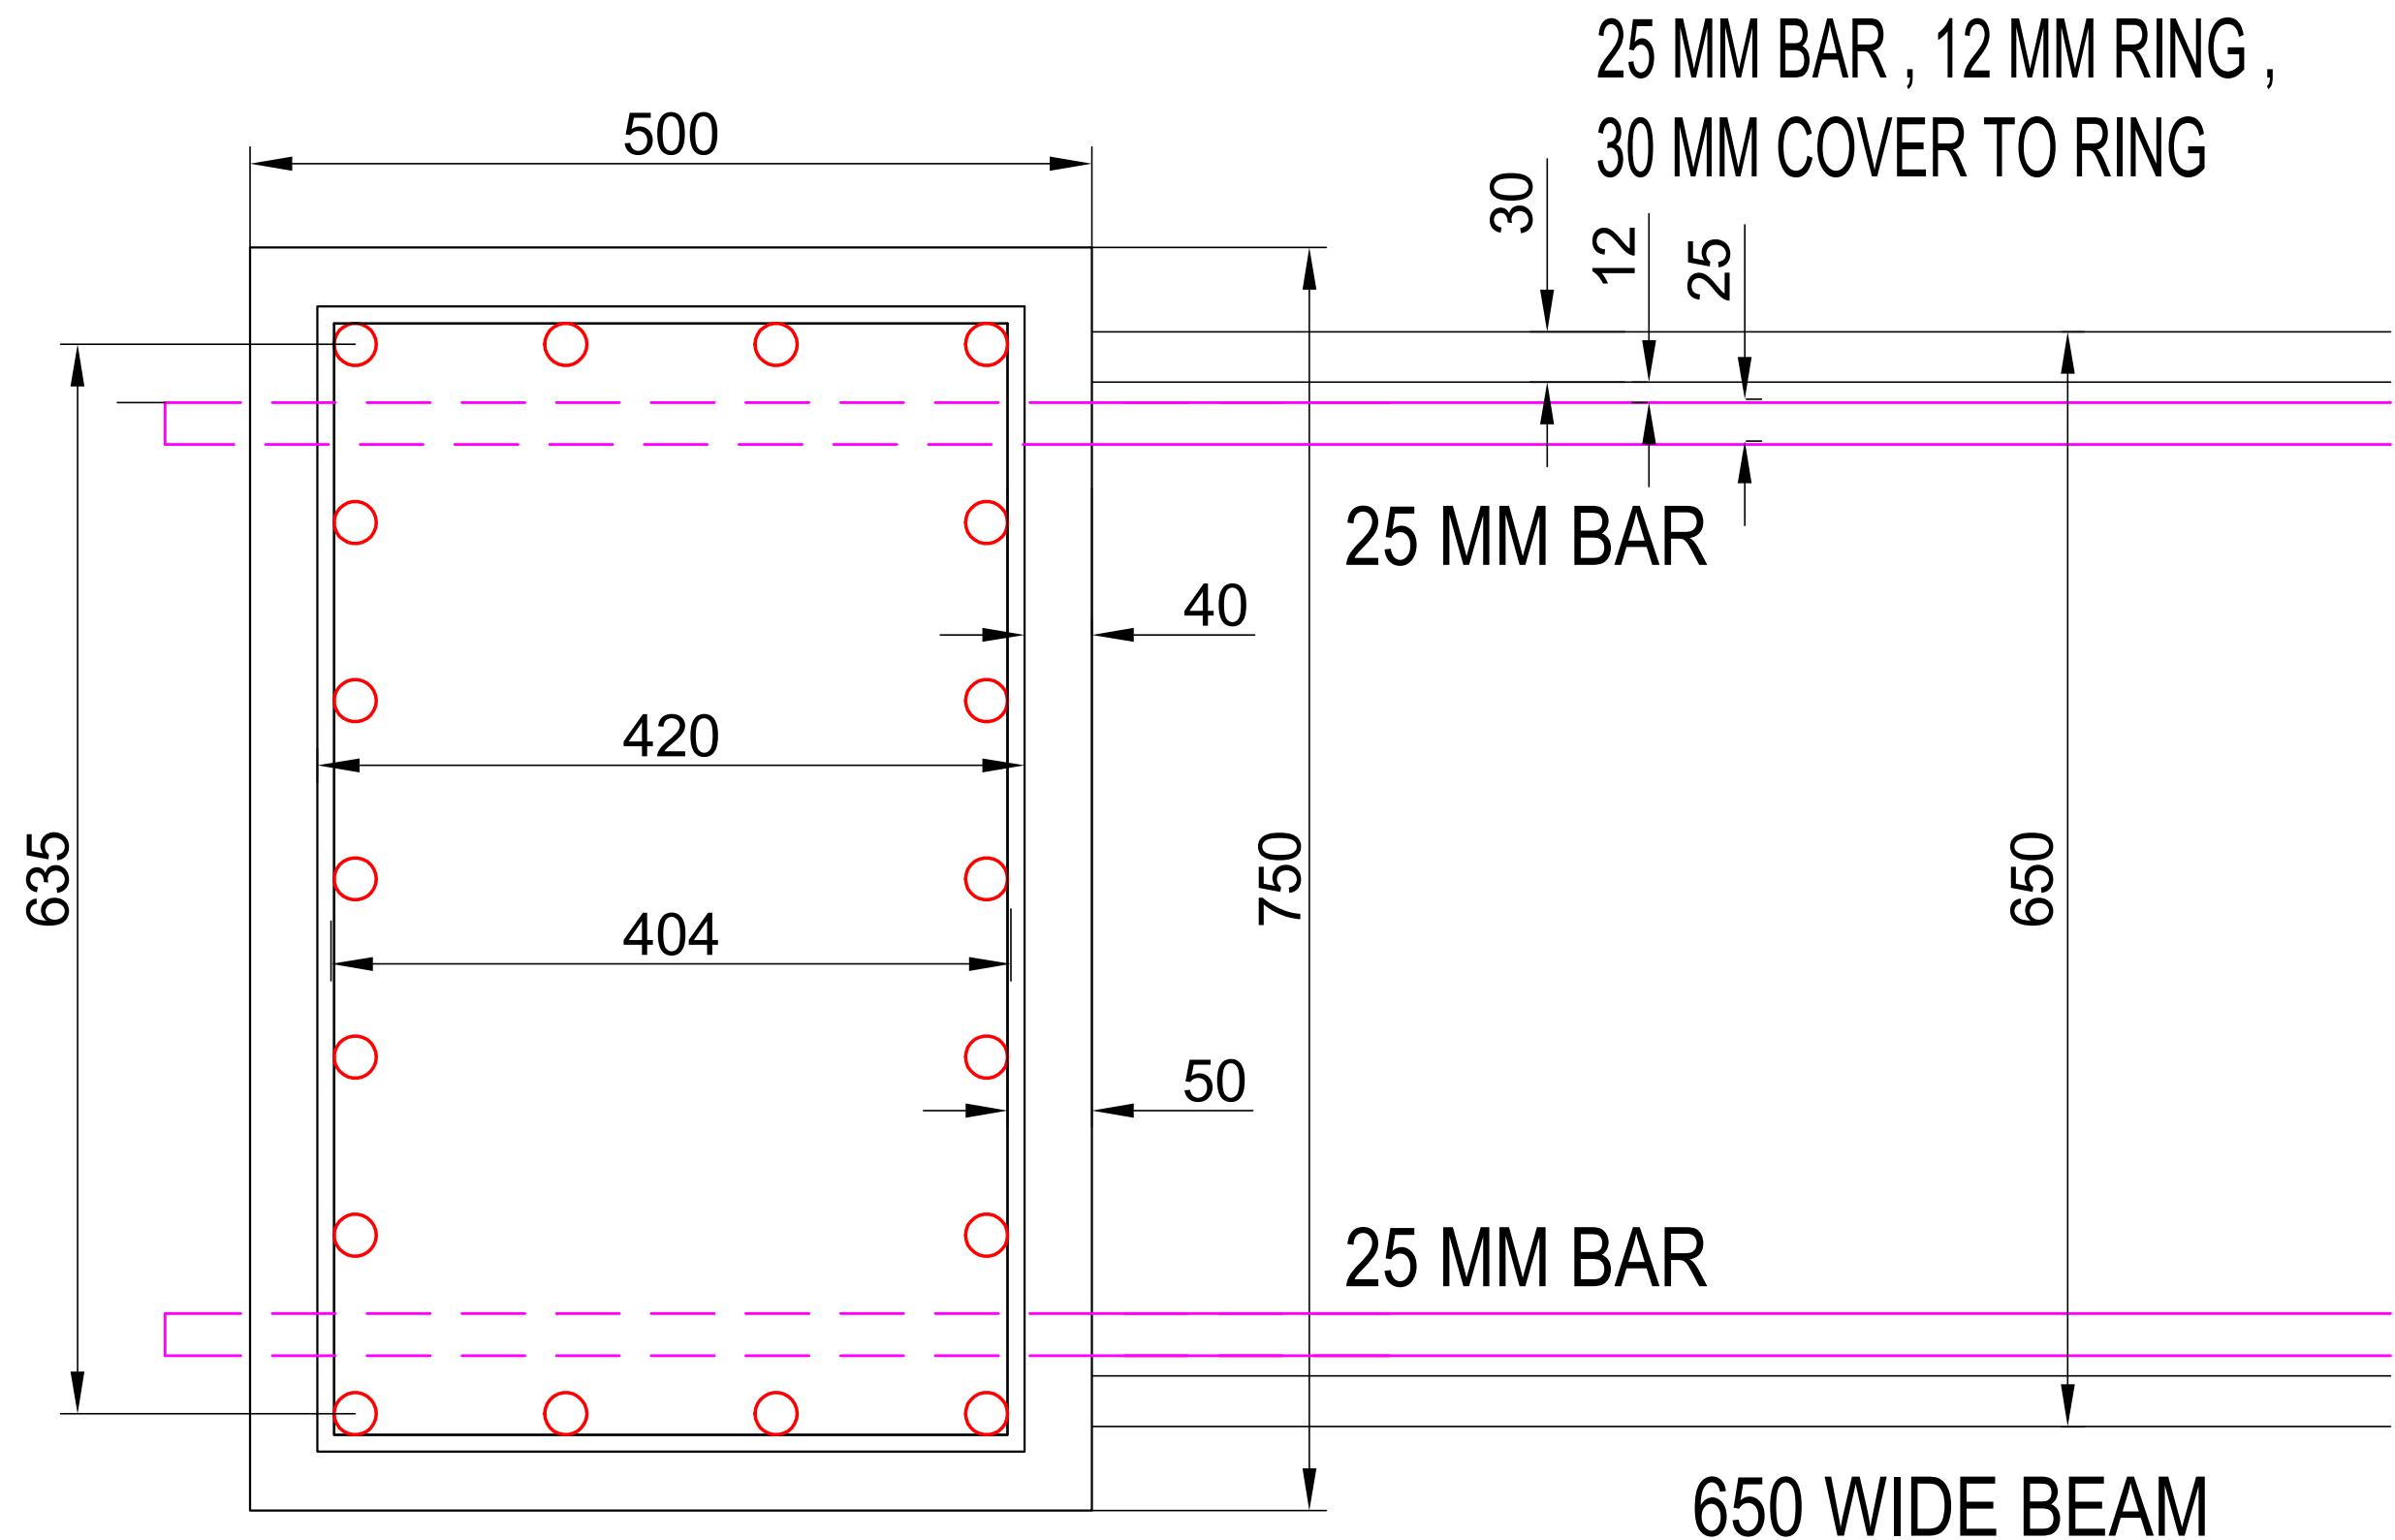

COLUMN

**PLAN ENSURING BEAM BARS GOING
EASILY INTO COLUMN**